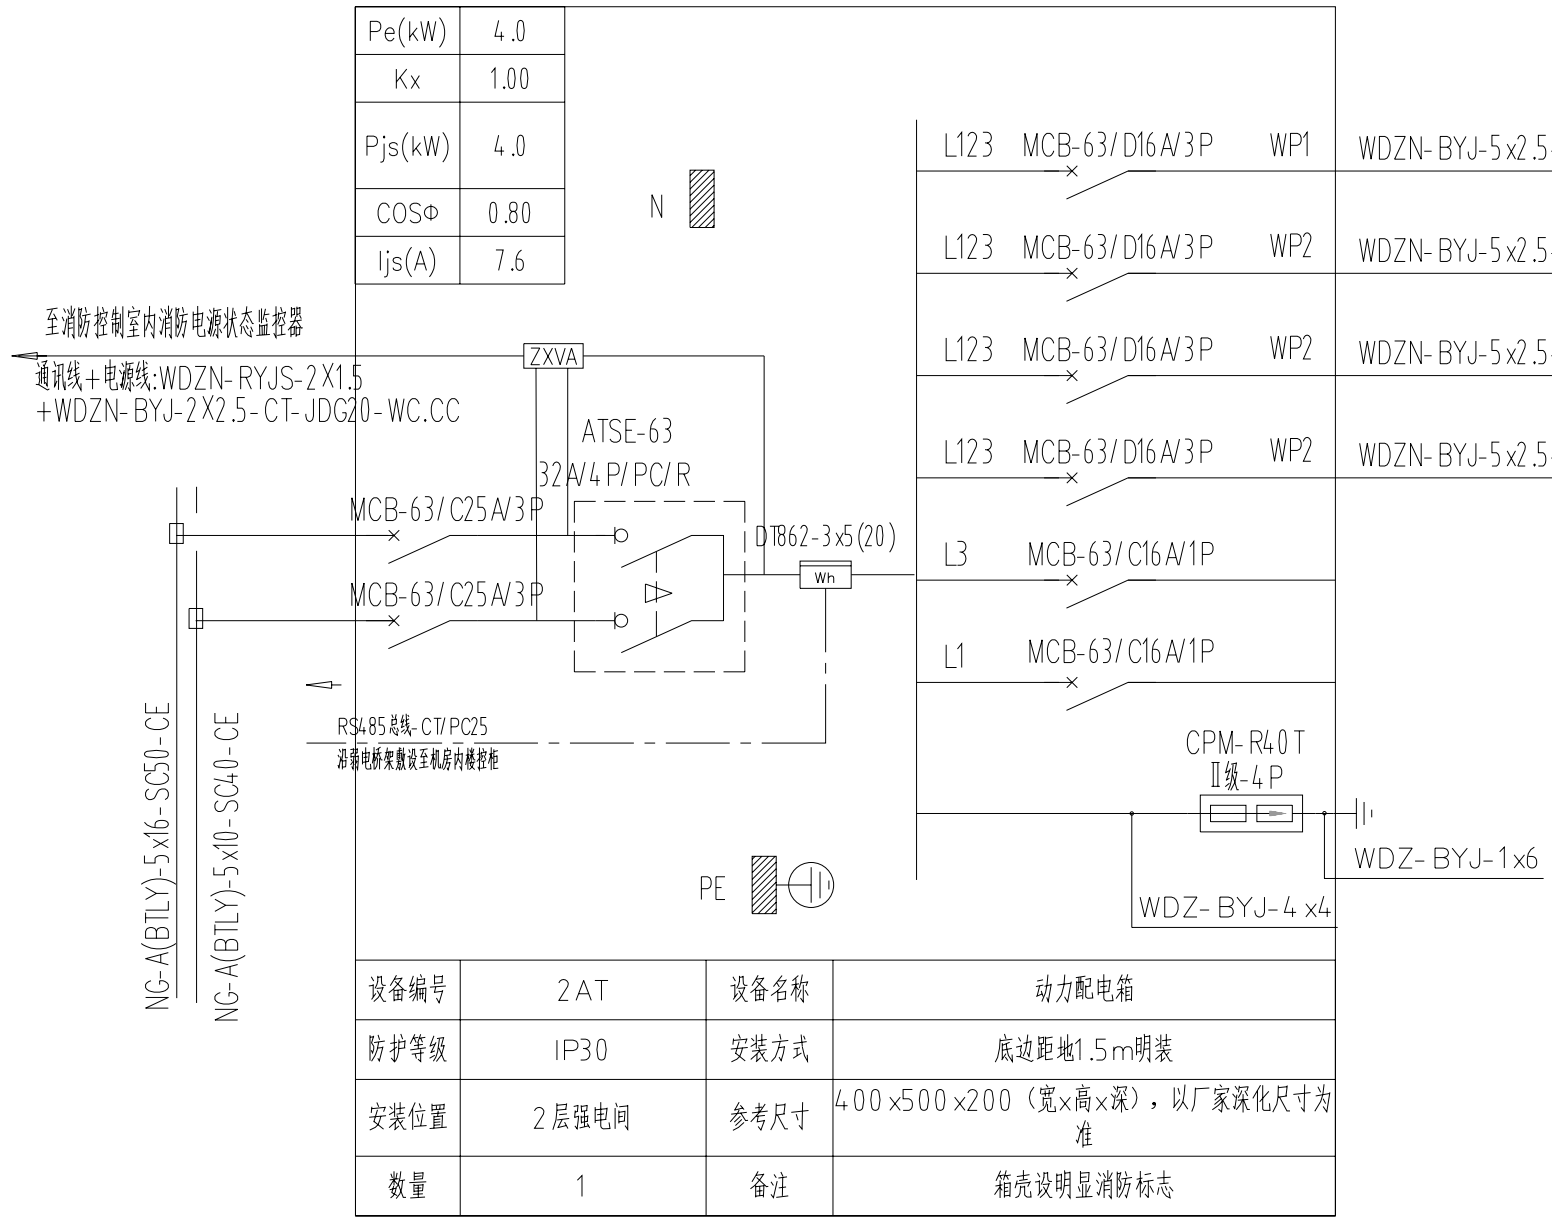

设备（名称）	功率（kW）
电动挡烟垂壁控制箱	1.0
电动挡烟垂壁控制箱	1.0
电动挡烟垂壁控制箱	1.0
电动挡烟垂壁控制箱	1.0
备用	--
备用	--

设备编号	2AT	设备名称	动力配电箱
防护等级	IP30	安装方式	底边距地1.5m明装
安装位置	2层强电间	参考尺寸	400x500x200（宽x高x深），以厂家深化尺寸为准
数量	1	备注	箱壳设明显消防标志