Pe(kW)	18.0
Kx	1.00
Pjs(kW)	18.0
COSΦ	0.85
Ijs(A)	32.2

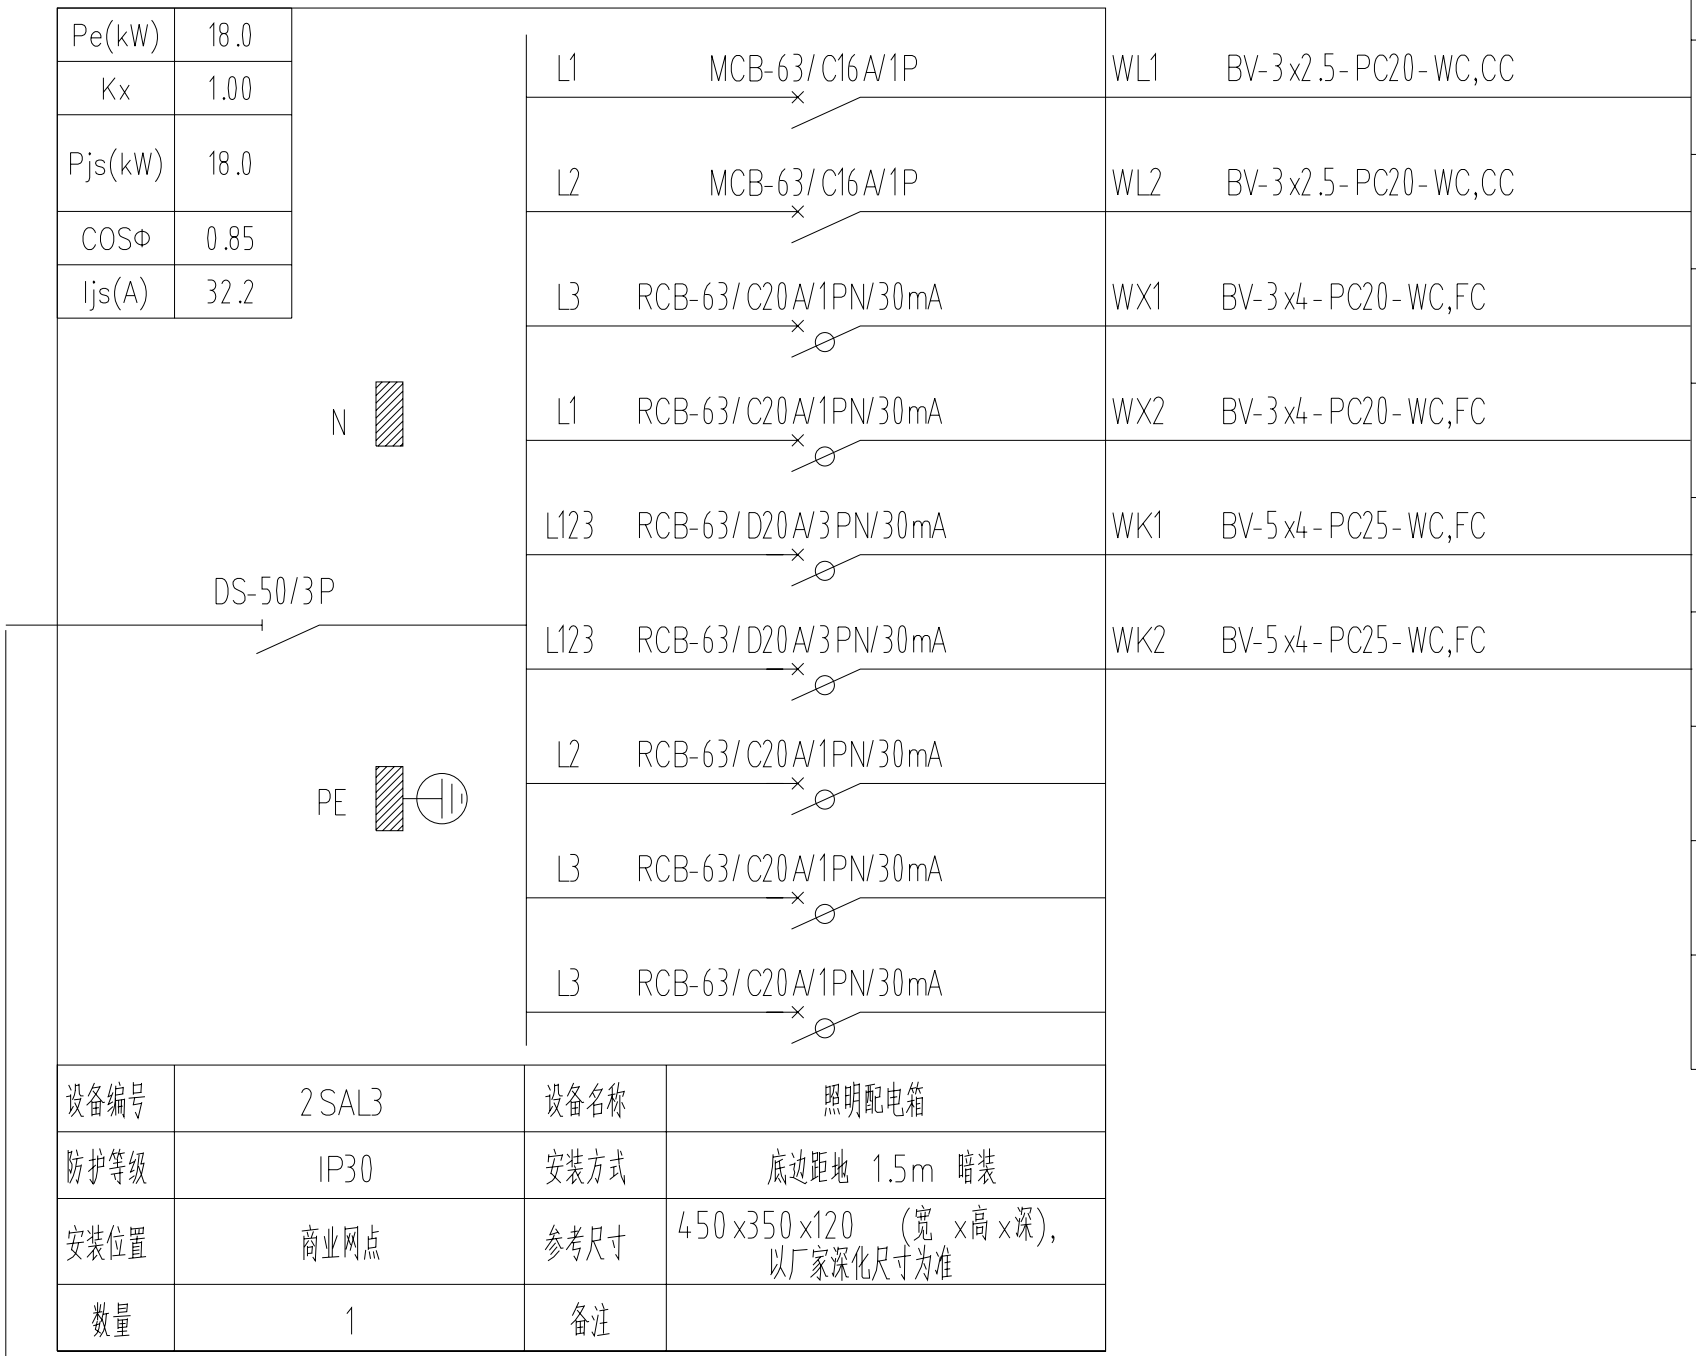

设备(名称)	功率(kW)
照明	1.0
照明	1.0
普通插座	2.0
普通插座	2.0
空调插座	4.0
空调插座	4.0
备用	--
备用	--
备用	--

设备编号	2SAL3	设备名称	照明配电箱
防护等级	IP30	安装方式	底边距地 1.5m 暗装
安装位置	商业网点	参考尺寸	450x350x120 (宽 x高 x深), 以厂家深化尺寸为准
数量	1	备注	

YJV-5x10-PC40-WC