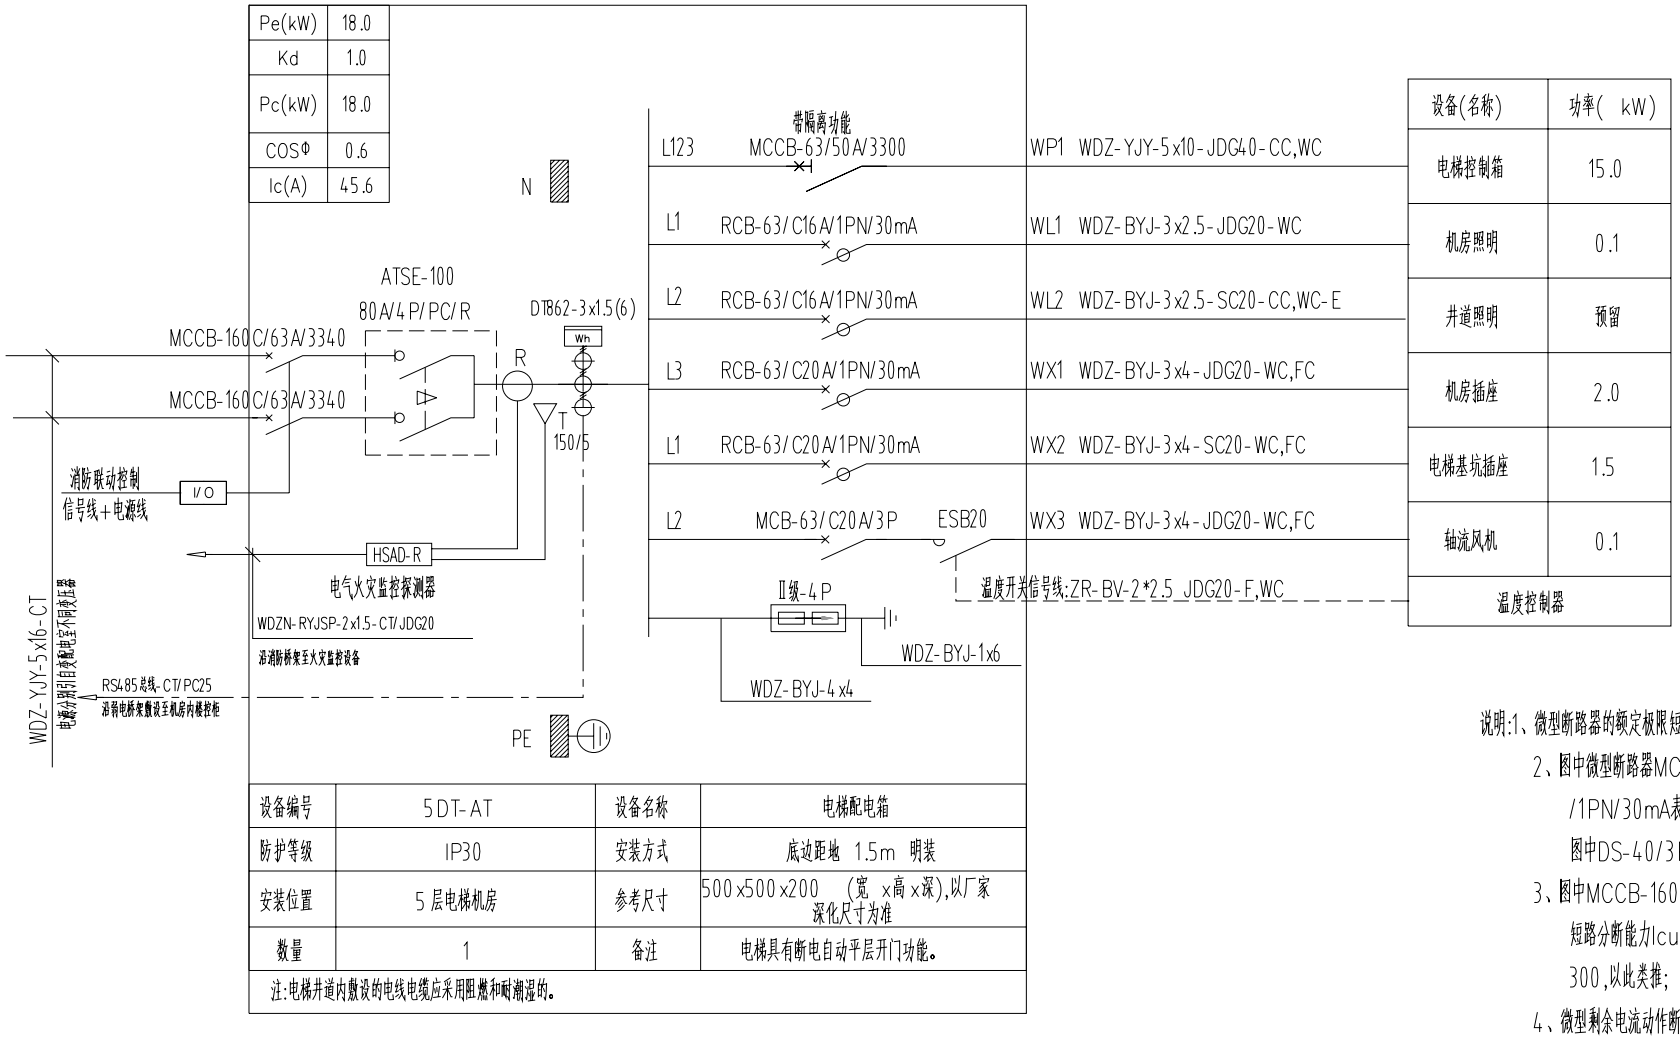


设备编号	5DT-AT	设备名称	电梯配电箱
防护等级	IP30	安装方式	底边距地 1.5m 明装
安装位置	5层电梯机房	参考尺寸	500x500x200 (宽 x高 x深),以厂家深化尺寸为准
数量	1	备注	电梯具有断电自动平层开门功能。

注:电梯井道内敷设的电线电缆应采用阻燃和耐潮湿的。

说明:1、微型断路器的额定极限短路分断能力(Icu)除注明外,均采用6 KA。

2、图中微型断路器MCB-63/C16A/1P表示1极16安C脱扣特性,以此类推;图中RCB-63/C20A/1PN/30mA表示1+N极16安C脱扣特性剩余电流动作断路器,30mA速断型,以此类推。
图中DS-40/3P表示3极40安隔离开关,以此类推。

3、图中MCCB-160L/125A/3300,表示带隔离功能塑壳断路器,壳架电流160A,额定极限短路分断能力Icu为L级标准型,整定电流为125A,而3300表示3极、脱扣器方式及内部附件代号为300,以此类推;

4、微型剩余电流动作断路器的额定剩余动作电流均为30mA,动作时间不大于0.1s;

5、消防控制回路中热元件仅作用于报警,不动作于跳闸。消防用电回路断路器不设过载保护。

5、配电箱数量仅供参考。